


The house to comply with
the National Construction Code (NCC)
2022 livable housing provisions
(accessibility and energy efficiency)

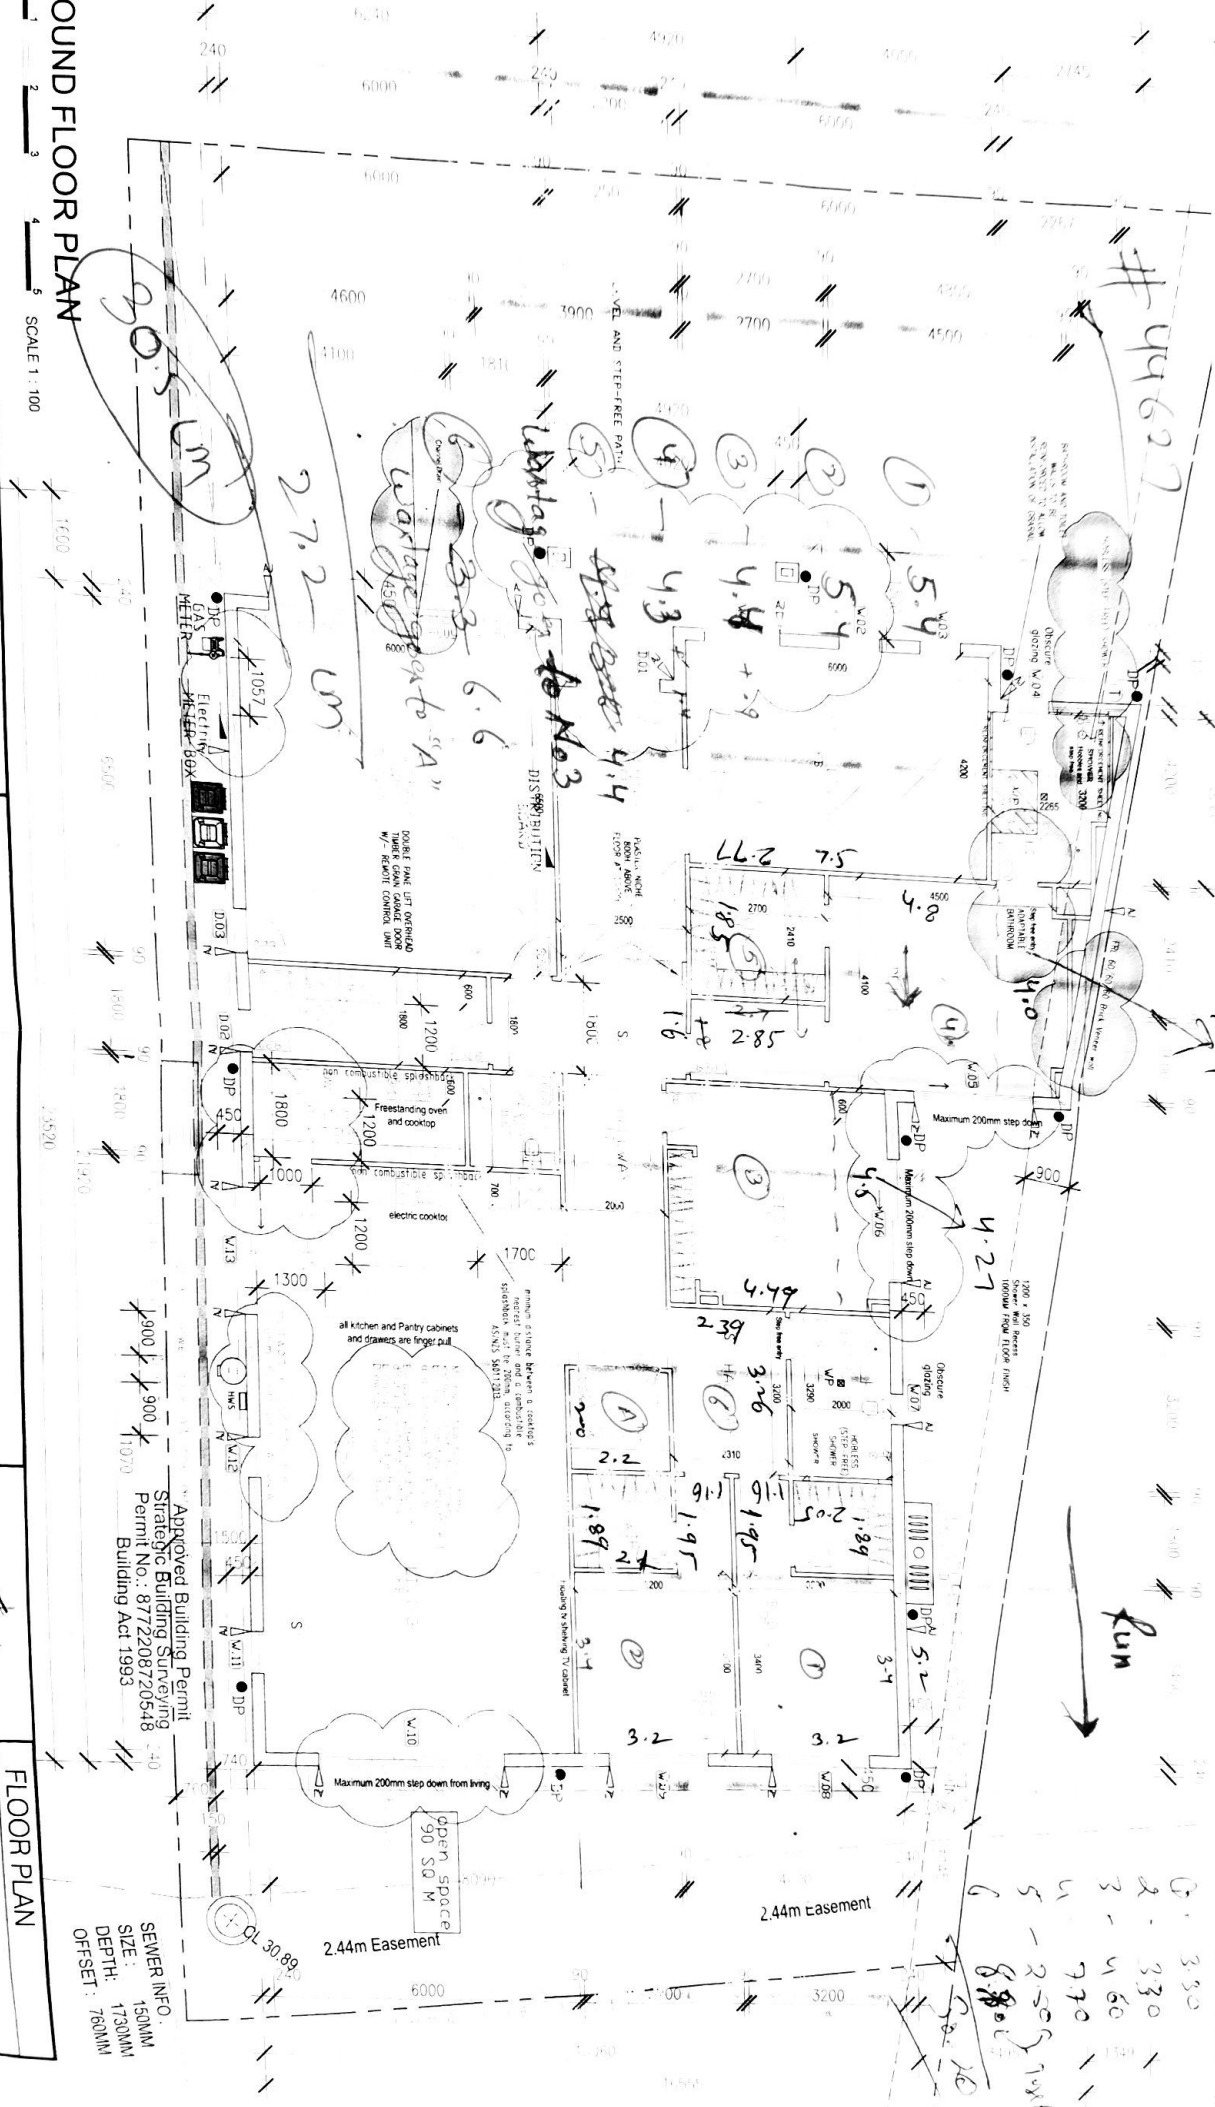

Akora Homes Pty Ltd
info@akorahomes.com.au
www.akorahomes.com.au
Factory 7, 17 Kitchen Road
Dandenong South 3175 VIC
ABN: 64 636 025 913

CONTRACTOR MUST VERIFY ALL DIMENSIONS AND LEVELS ON SITE TO COMMENCEMENT OF ANY WORKS OR MAKING ANY SHOP DRAWINGS
DO NOT SCALE DRAWINGS
ALWAYS USE WRITTEN DIMENSIONS
THESE PLANS ARE TO BE READ IN CONJUNCTION WITH AND COMPLY WITH ALL TO DEVELOPERS

CLIENT
Barkat Ali
PROPOSED SINGLE STORY HOUSE
5 BARTON STREET DANDENONG NORTH 3175

ADDRESS

**AKORA HOMES**

Consent Action Copy
CAO Reference
Date: 21.10.2025
Scale 1:100
Drawing No. AR-02

Drawn Naid
Sheet 04

Approved Building Permit
Strategic Building Surveying
Permit No.: 8772208720548
Building Act 1993

SEWER INFO.
SIZE: 150MM
DEPTH: 1730MM
OFFSET: 780MM