


Name and Address		Subfloor		Doors		Trims		Dunlop Underlay		Stairs		Date		Measured By	
#45240		Wood		✓	Furniture	?	Type	Gld		16		12/06/28		K.H	
First floor		Concrete			Existing Covering	X	Size	Smooth Edge		FloorShield					
							Total	☒ Standard ☐ Architectural		☐ Yes ☐ No					

Ground floor


Notes
 => Subfloor slates
 Entry = 11.60
 Din + Kitchen 22.68
 + 13.15
 Hallway = 3
 Laundry = 8.45
 Toilet & Shower not included

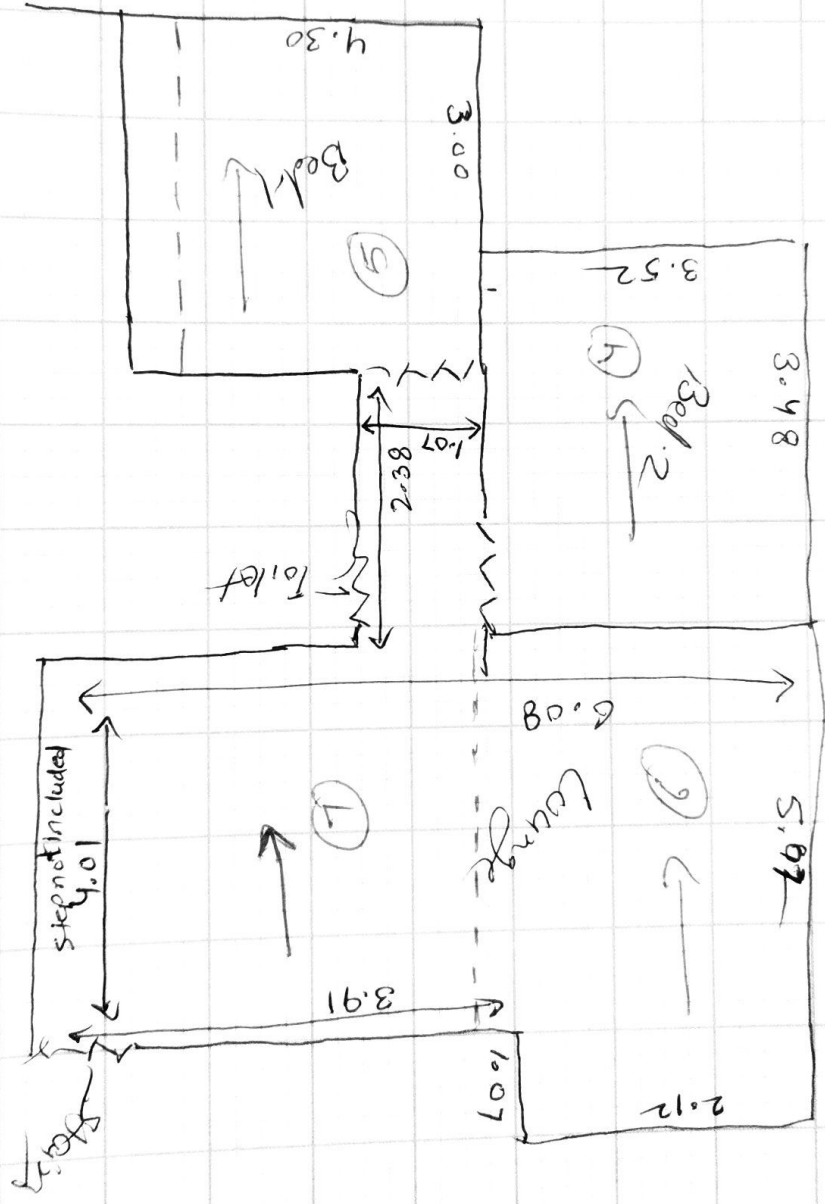

Name and Address		Subfloor		Doors		Trims		Dunlop Underlay		Stairs		Date		Measured By	
		Wood		Furniture		Type		Green		FloorShield					
		Concrete		Existing Covering		Size		Smooth Edge		☐ Standard ☐ Architectural		☐ Yes ☐ No			
# 45830						Total								K.H	

Kitchen - $4.91 \times 2.90 = 15.63 \text{ m}^2$

Laundry - $1.76 \times 2.16 = 7.86 \text{ m}^2$

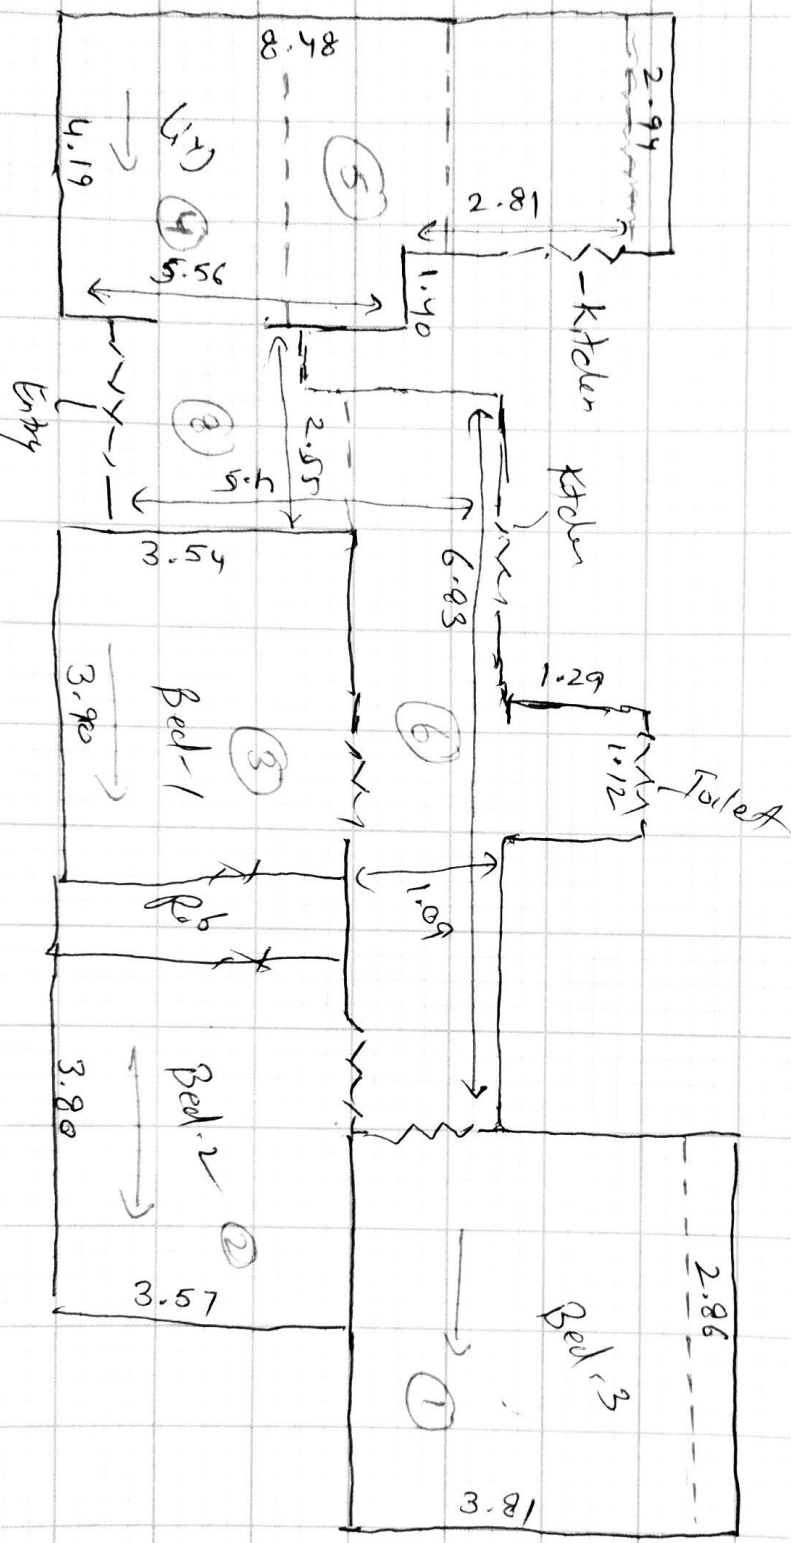

Notes

- ① 2.9
 - ② - 3.9
 - ③ - 4.0
 - ④ - 4.3
 - ⑤ - 4.3
 - ⑥ - 6.9
 - ⑦ - 6.8
 - ⑧ - 2.6
- Wentage goes to 1 & 5, 7
- 35.76m