#46117

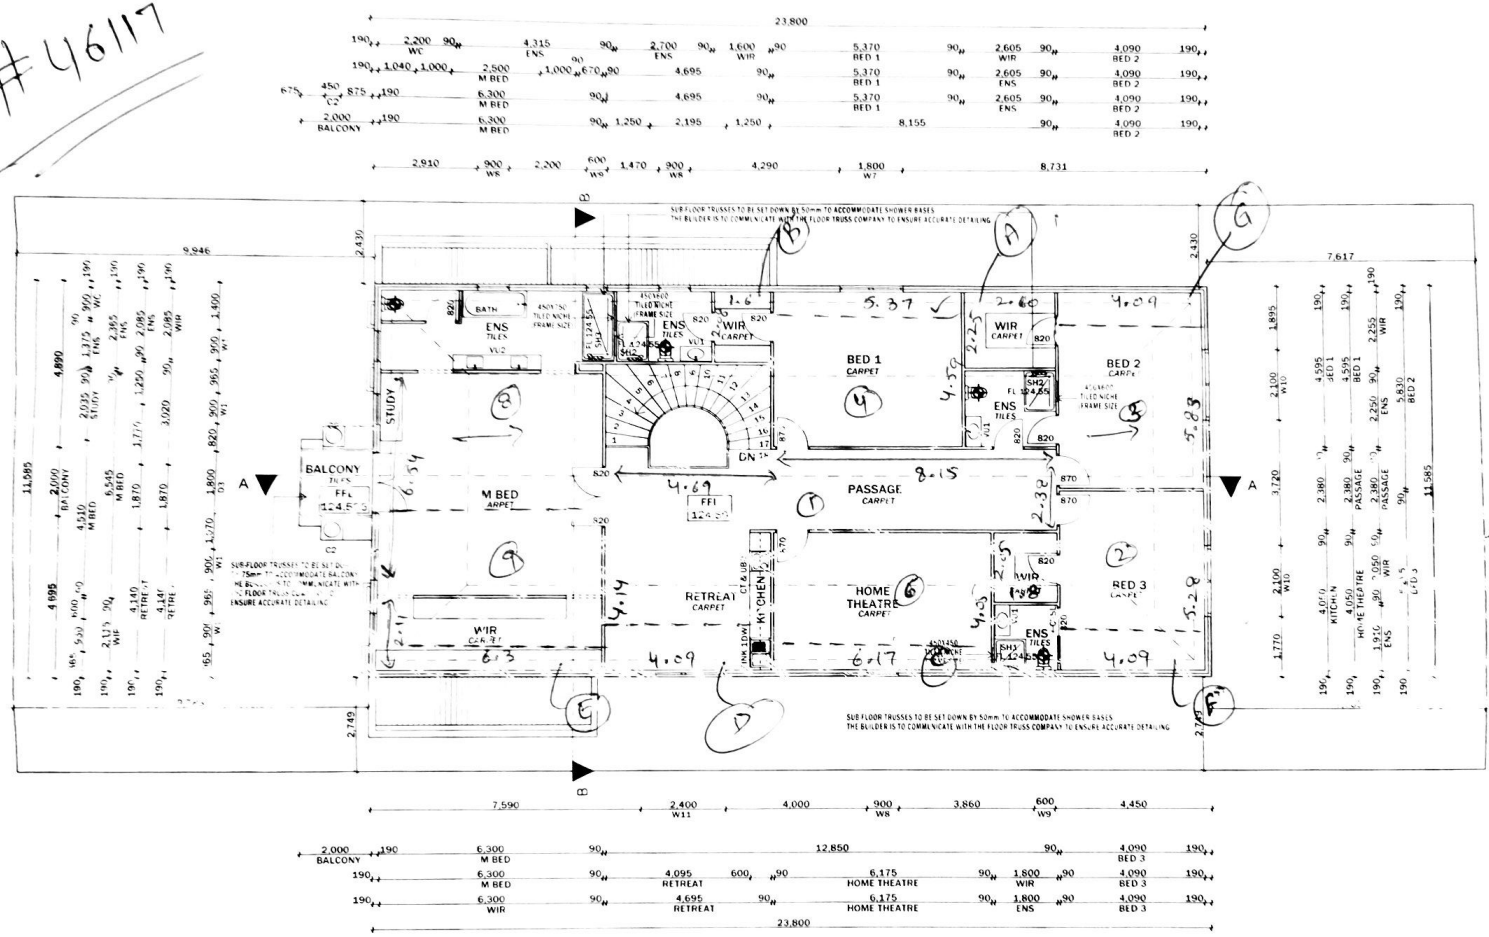

(1) - 13.0 wastage goes to C "

(2) - 6.0

(3) - 4.1

(4) - 5.5

(5) - 4.3

for A-B & wastage goes to No 4.

(6) - 6.3

(7) - 4.2

(8) - 6.4

(9) - 6.4

(10) - 6.4 for E & F

(11) - 5.9

(12) - 5.9 for "G" & "H"

CONSTRUCTION ISSUE

COPYRIGHT WARNING - CK DESIGN GROUP (PVT) LTD

COPYRIGHT THIS DOCUMENT REMAINS THE PROPERTY OF CK DESIGN GROUP (PVT) LTD. THIS DOCUMENT, DRAWING IS PROTECTED BY FEDERAL COPYRIGHT LAW. COPYING IN ANY SHAPE OF FORM, IN WHOLE OR PART WITHOUT THE WRITTEN AUTHORISATION OF THE DRAFTING PRACTITIONER AND / OR AUTHOR REFERRED TO IS STRICTLY PROHIBITED. CIVIL PROCEEDINGS, CLAIMING DAMAGES OR OTHER REMEDIES MAY BE BROUGHT AGAINST PERSONS FOUND COPYING THIS DOCUMENT WITHOUT PERMISSION.

CK DESIGN GROUP

PROJECT TITLE
PROPOSED DOUBLE STOREY DWELLING AT 32, MILLOO CRESCENT, MOUNT WAVERLEY.

~~74.4~~ LM

DRAWING TITLE
FIRST FLOOR PLAN

DRAWING NO	CKD.PP.SS.4		
DESIGN BY	C.K.	DATE	05.2023
CHECKED BY	C.K.	SCALE	1:100
VERSION	01	DRAWN	Y.C

BUILDING PRACTITIONER
Chamith kellapatha

REV	DESCRIPTION	DATE
01		28.2023

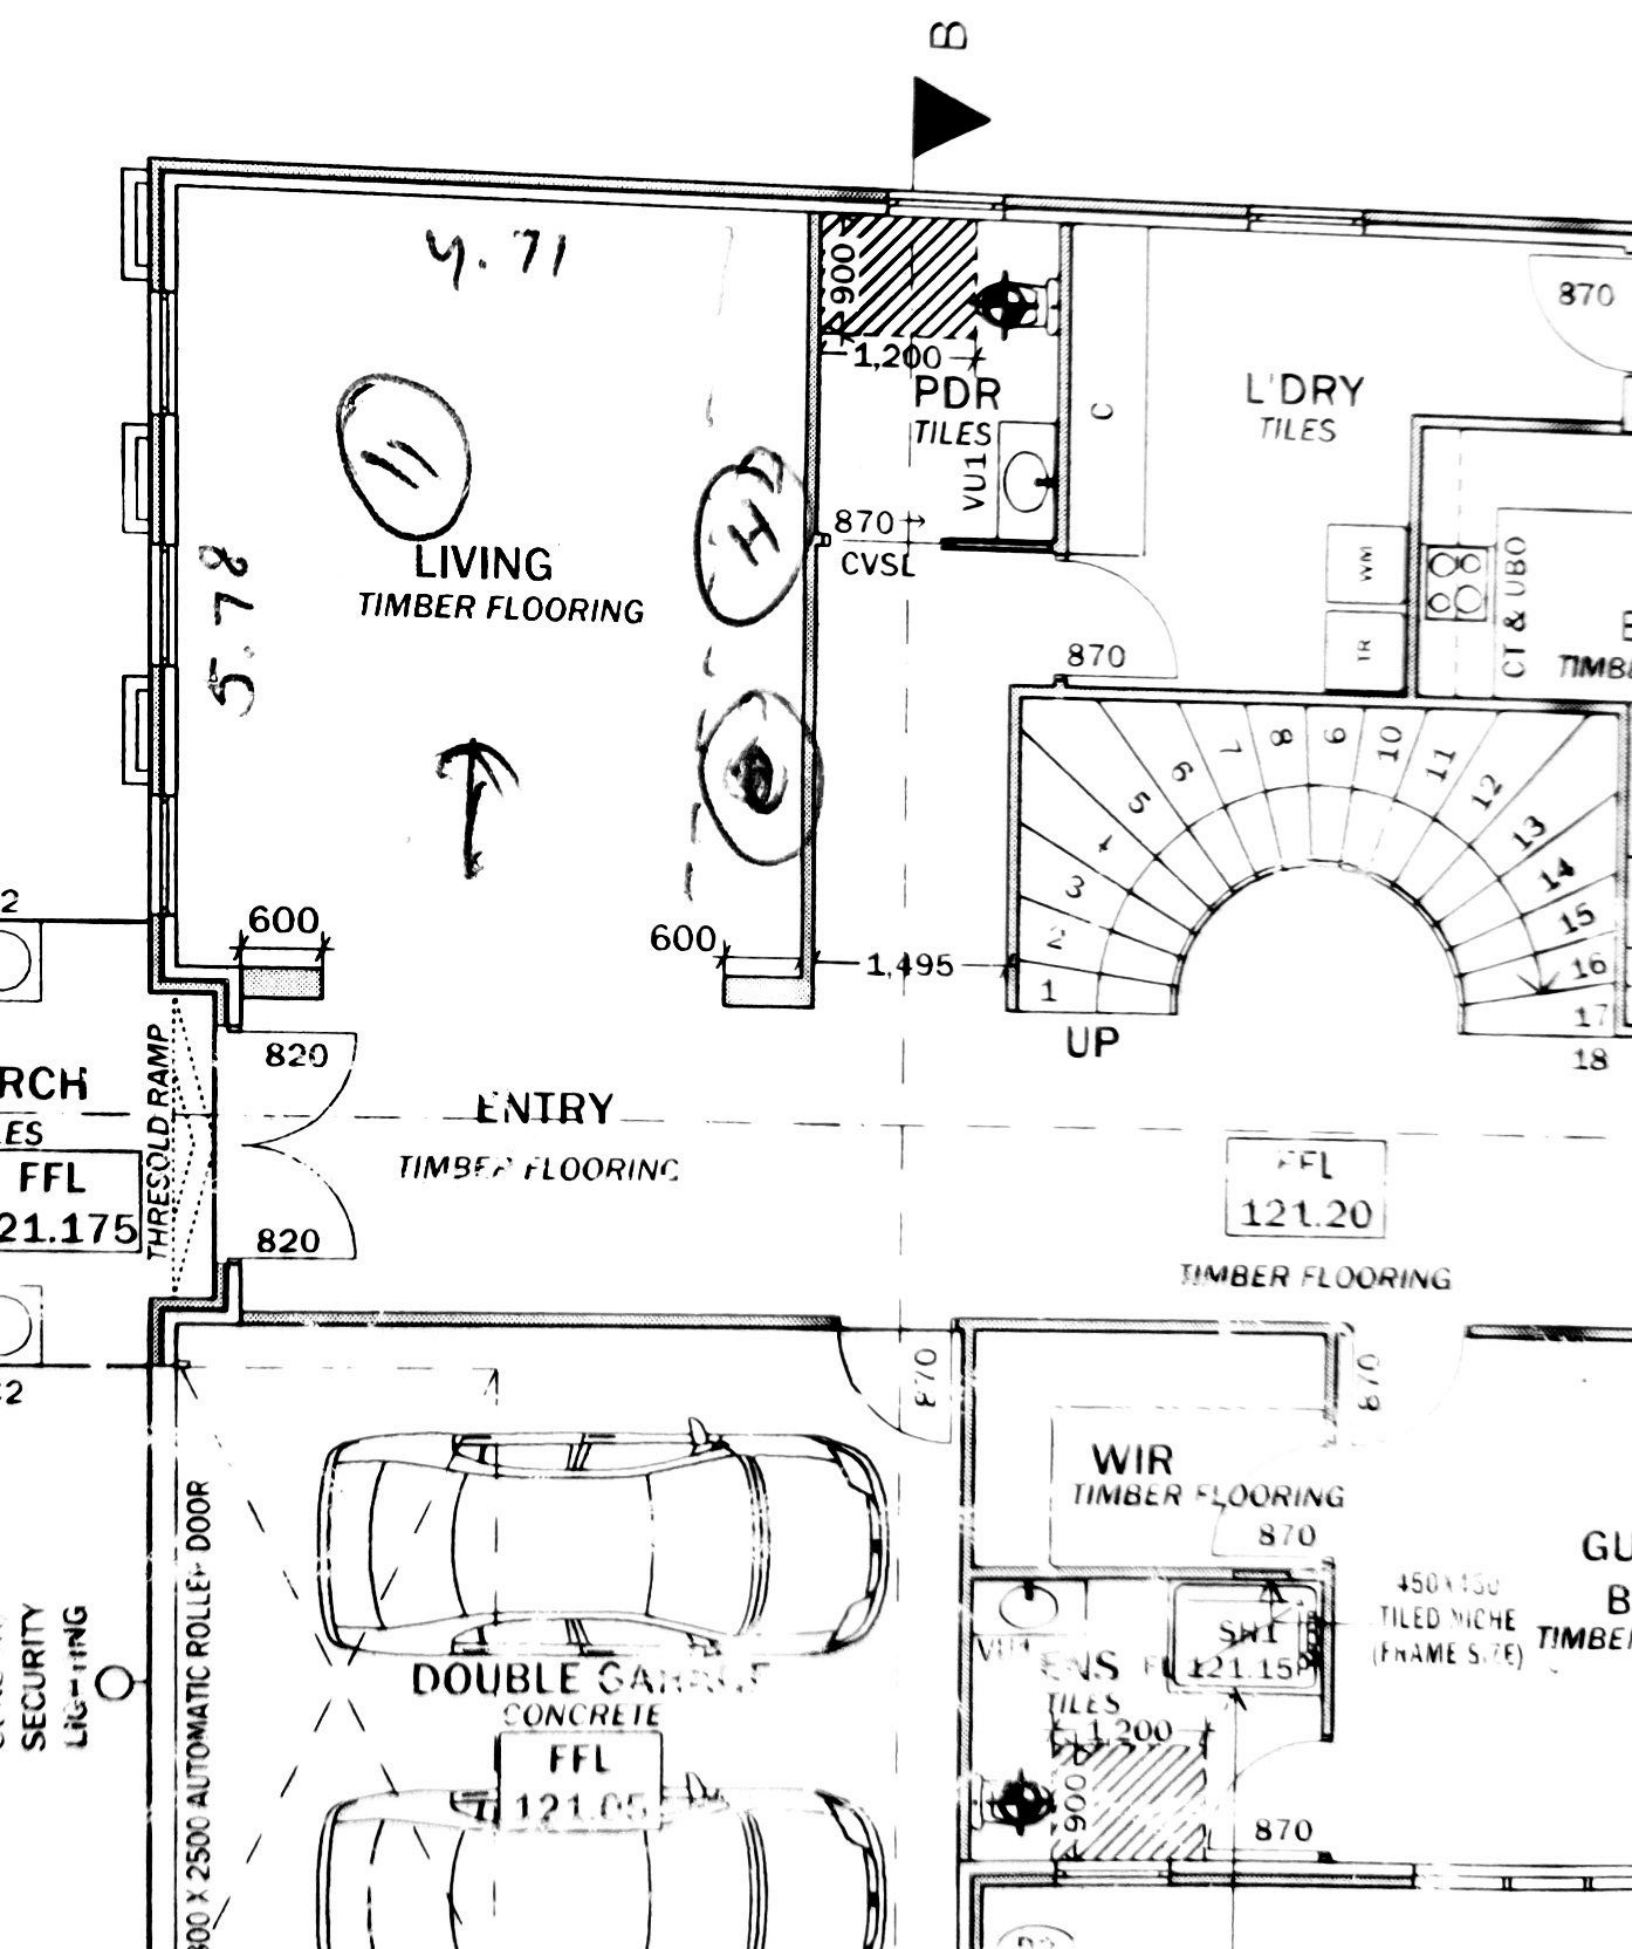
B
4.71
5.78
LIVING
TIMBER FLOORING
900
1,200
PDR
TILES
VU1
C
870
CVSL
L'DRY
TILES
WM
TR
CT & UBO
870
600
600
1,495
1
2
3
4
5
6
7
8
9
10
11
12
13
14
15
16
17
18
UP
820
ENTRY
TIMBER FLOORING
THRESOLD RAMP
820
FFL
121.20
TIMBER FLOORING
RCH
ES
FFL
21.175
SECURITY
LIGHTING
DOUBLE GARAGE
CONCRETE
FFL
121.05
870
WIR
TIMBER FLOORING
870
SH1
121.15
TILES
1,200
900
870
450 X 150
TILED NICHE
(FRAME S.7E)
GU
B
TIMBE
800 X 2500 AUTOMATIC ROLLER DOOR